



1 Sofa table, isometric

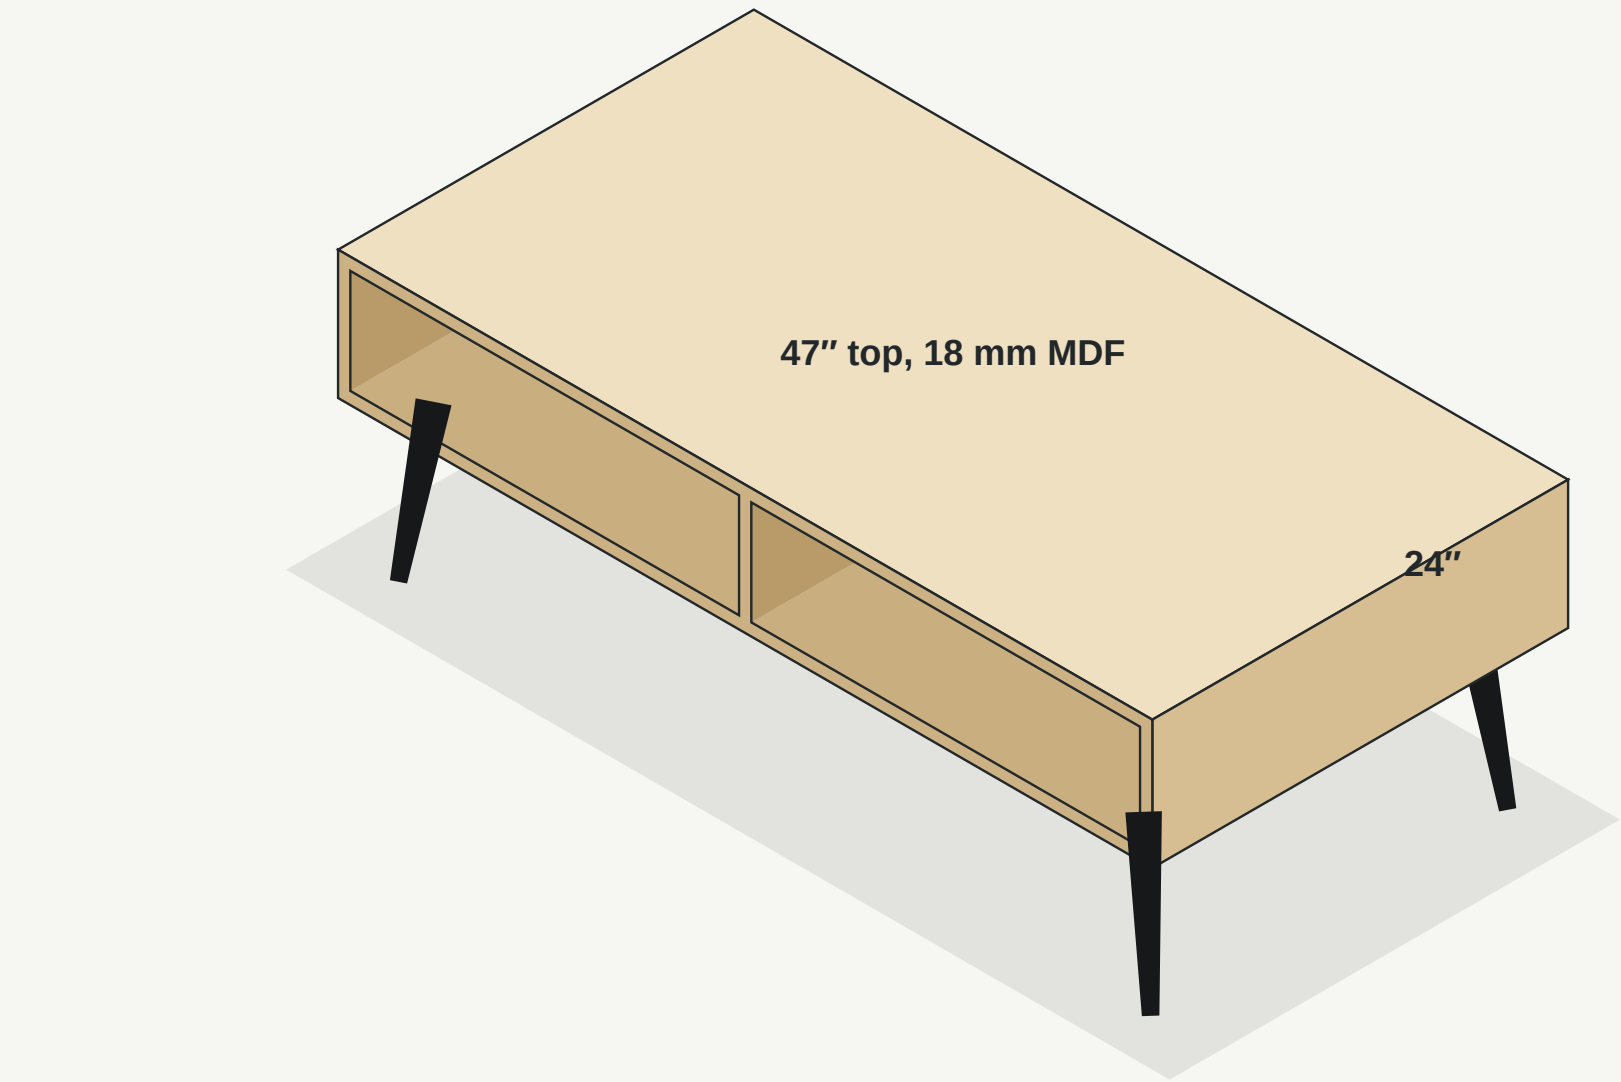


two equal open compartments, four splayed black legs

3 Front elevation

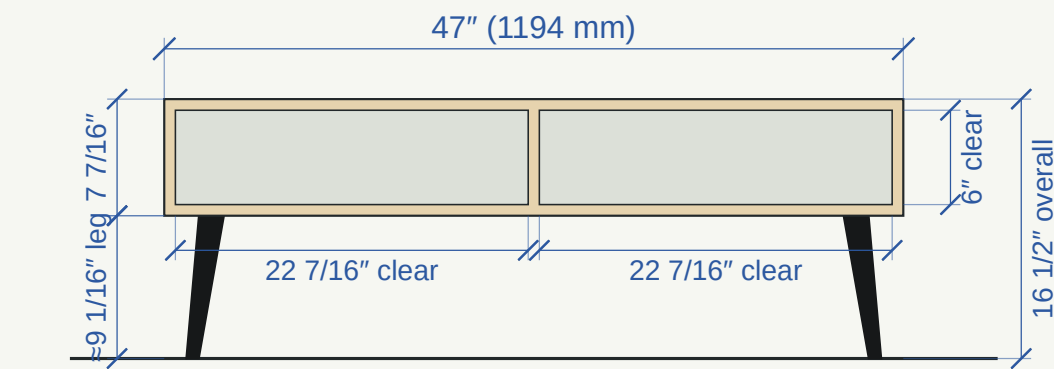


1 : 8 approx.

4 Top plan

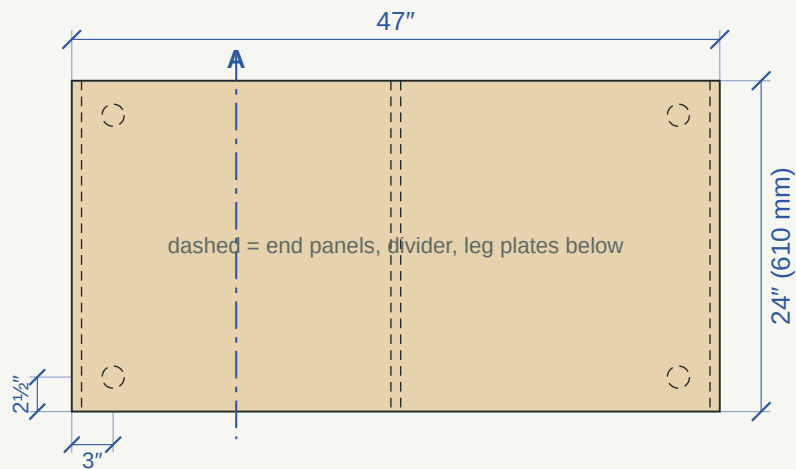


hidden lines dashed

2 Bedroom floor plan, 14' x 11'-6"

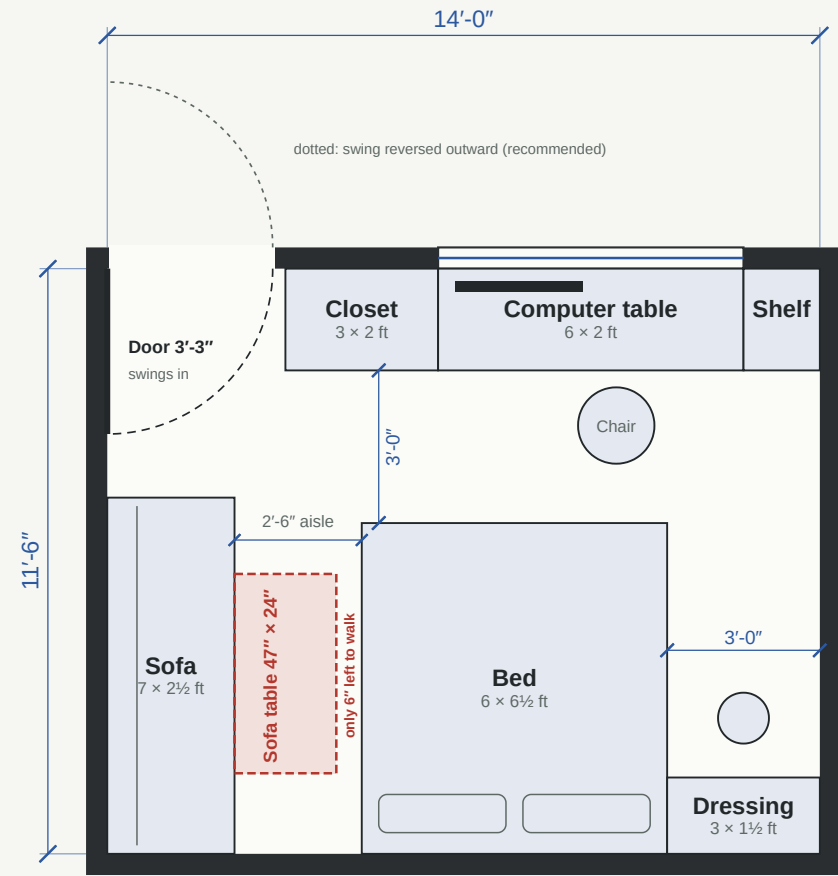


5 Section A-A

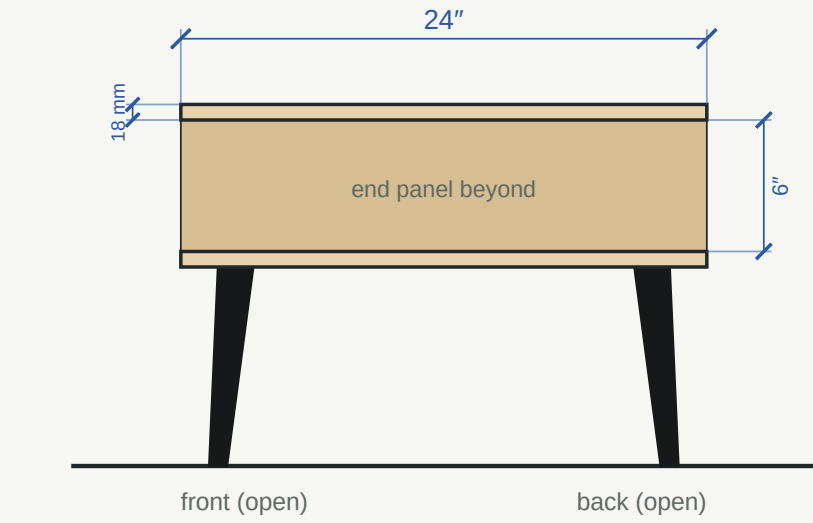

through one compartment

6 Sheet 1, stood upright: table + doors

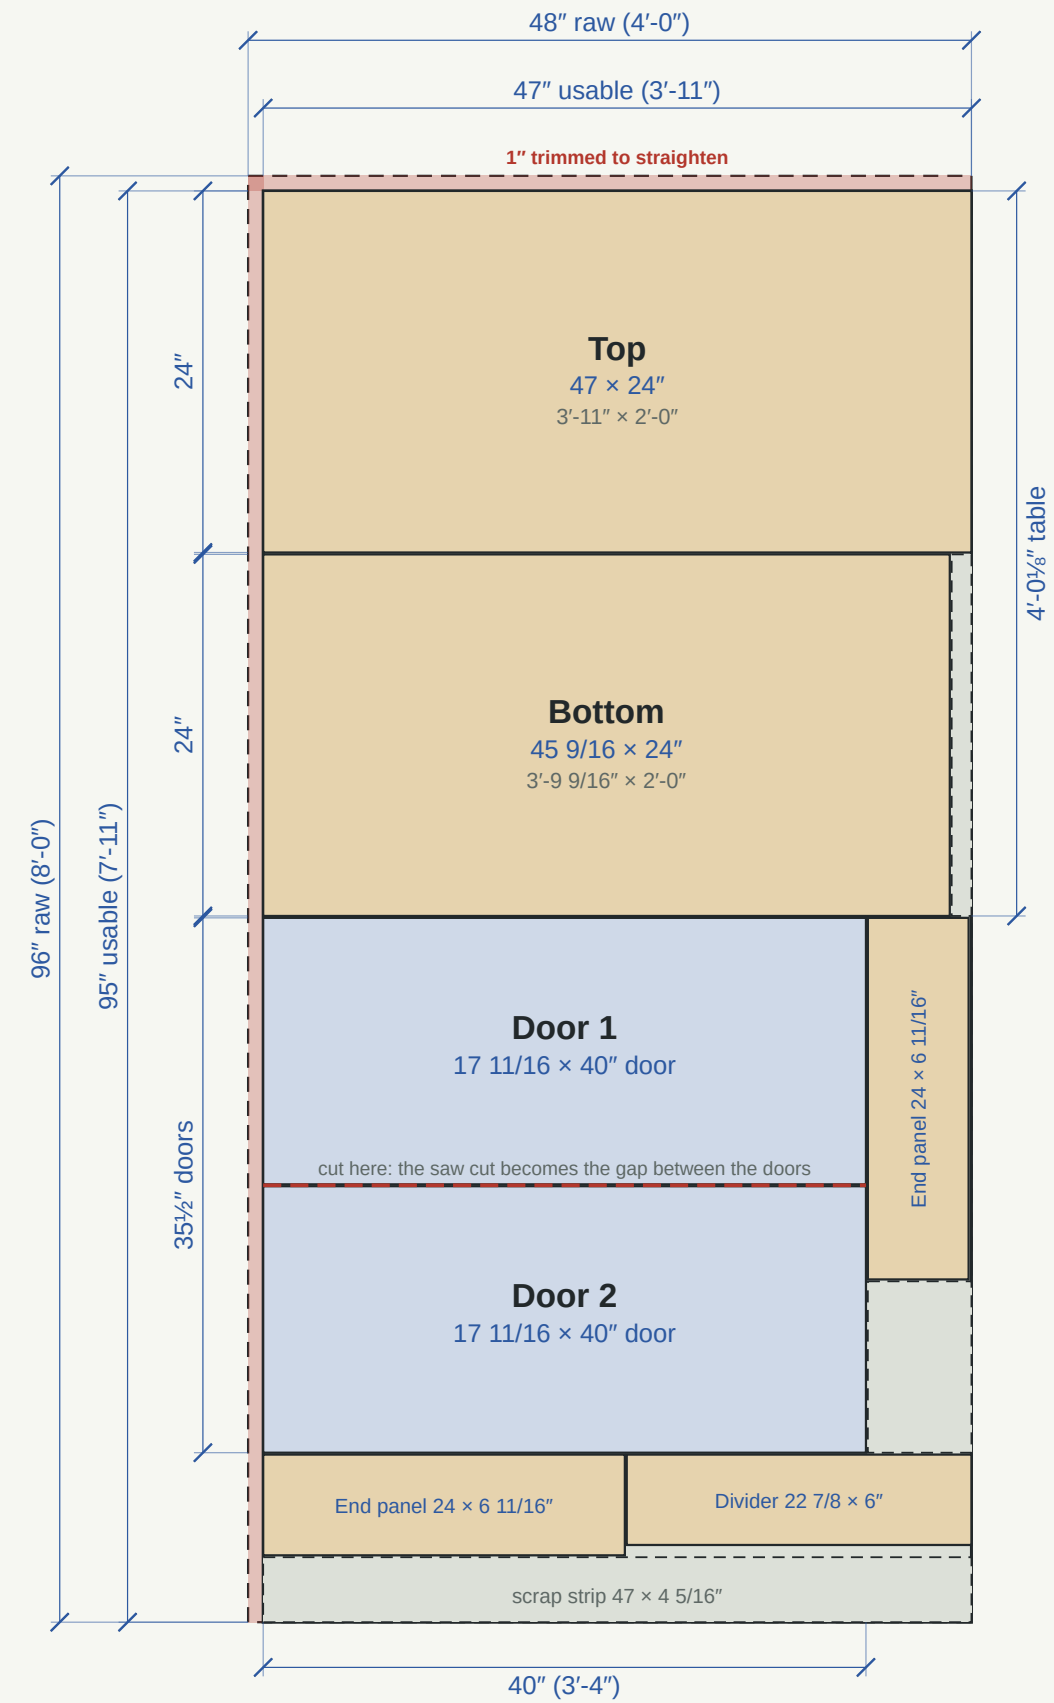

1/8 inch saw cuts allowed

Cut list, sheet 1, 18 mm MDF

Part	Qty	Size (in)	Size (mm)
Top	1	47 x 24 (3'-11" x 2')	1194 x 610
Bottom, fits between ends	1	45 9/16 x 24	1158 x 610
End panels	2	6 11/16 x 24	170 x 610
Centre divider, set back 1 1/8"	1	6 x 22 7/8	152 x 581
Doors	2	17 11/16 x 40 (3'-4")	449 x 1016
Black tapered legs, angled plates	4	≈ 9 1/16 long	≈ 231
Edge tape, table + doors	1 roll	≈ 14 m used, buy 16 m	

The top runs the full 47" and sits on the end panels; the bottom fits between them, which leaves some margin in case the trim is a little more than 1". Each opening is 22 7/16" (570 mm) wide x 6" tall.

7 What fits where

sheet 2 drawn once the gun height is known

Notes

- Overall height 16½" is assumed.** Measure your sofa's cushion height, subtract 1–2", then subtract the 7 7/16" box. That is your leg length.
- Tape every visible edge. Tape adds under 1 mm, so it doesn't change any size on this sheet.
- Table is now 47" long** so the top and bottom stack across the upright sheet. If the cutter trims a hair more than 1", the top just comes out a hair shorter.
- Top onto ends and divider: 8 mm dowels and glue, so the top stays clean. Bottom into ends: confirmat screws through the end panels, with cover caps, plus glue. Pre-drill everything.
- The divider is 1½" shorter than the table depth so it fits the sheet; set it back from the front, like in the photo.
- Mount legs on angled plates, set 3" in from the ends and 2½" in from the long edges, for the splay shown.
- Ironing only on a heat-resistant pad, never direct on the laminate.
- Placement clash: with the 6'-wide bed the sofa-to-bed aisle is 2'-6". The 24"-deep table leaves only 6" to walk past (view 2).**

Sofa table, doors & bedroom layout

One sheet combining the table, the doors, the cutting plan and the master bedroom plan.

Table	47 x 24 x 16½" (assumed)
Clear openings	6" high, 2 equal
Material	18 mm MDF, taped edges, black legs
Room	14'-0" x 11'-6", 161 sq ft
Bed	6'-0" wide x 6'-6" long
Sheet	one 8' x 4' upright, trimmed to 47 x 95"; gun box on a second sheet
Units	inches unless noted
Date	Sheet 1 of 1, 23 Sep 2026

board doors legs dimensions clash